APD DEMO P .APD.

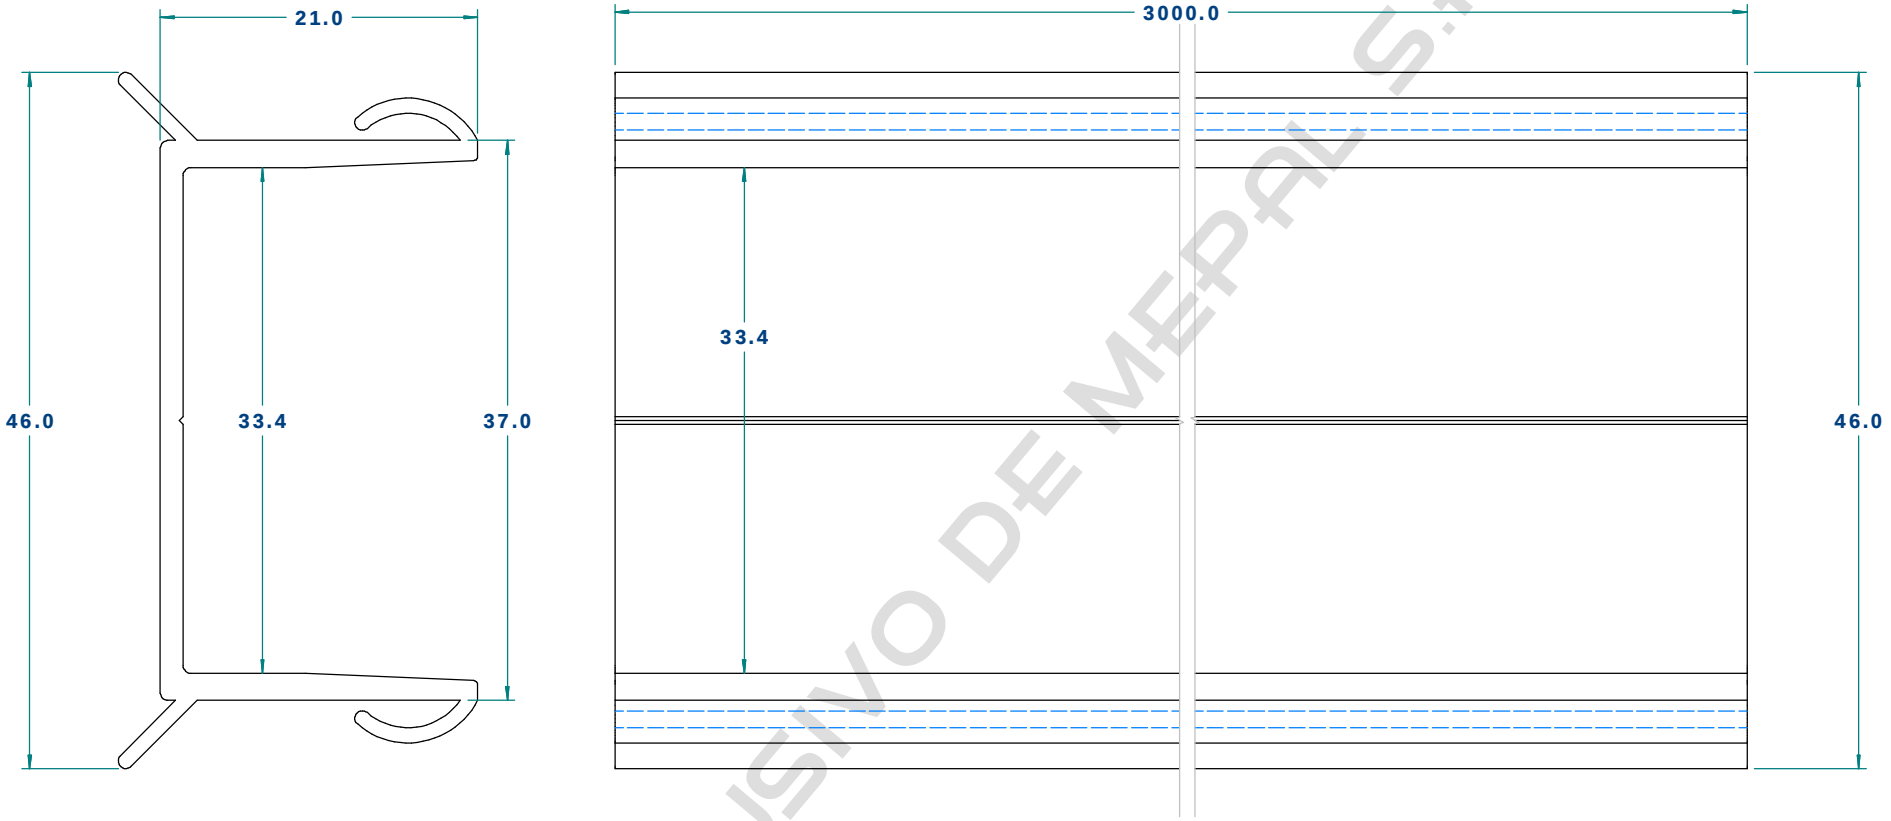

USO EXCLUSIVO DE MEPAL S.A.

Nombre : Perfil llegadas

Material : Plástico coextruido Ref. SI3302P0201

Acabado. : Crudo

Cantidad. : 1 Unidad

T.C. : 3000.0

Nota _1. Ver plano de materia prima MPR-060-055

MEPAL
UNA EMPRESA CARVAJAL

FIRMA DE APROBACION

DIMENSIONES EN MILIMETROS
NO MEDIR SOBRE PLANO

DISEÑO: Diseño & Desarrollo — FECHA: 02/09/2008
DIBUJO: *Orlando Solis Cadena* — FECHA: 01/10/2008
ESCALA: 2:1
ARCHIVO: VTAC010001

TOLERANCIAS NO INDICADAS	
DIMENSIONALES	` 1.0 mm
TROQUELADOS	` 0.2 mm
PERFORACIONES	` 0.2 mm
ANGULARES	` 1.0°
DESPUNTES	` 0.3 mm
PIVATIC - TRUMPF	` 0.2 mm

REVISION	NOTA DE ING.	FECHA	NOMBRE
00	086-08	2009-02-06	E.B.

LINEA: V E T R O
TITULO: PERFIL LLEGADA
PISO, TECHO Y/O PARED

CODIGO: S.C.
PLANO N°: VTAC-010-001 Rev00

LA INFORMACION TECNICA CONTENIDA EN ESTE PLANO ES PROPIEDAD DE MEPAL ESTA INFORMACION SOLO PUEDE SER USADA POR TERCEROS CON PREVIA AUTORIZACION ESCRITA DE MEPAL

Rev. 07, Oct. 07/05

Created with Print2PDF. To remove this line, buy a license at: http://www.software602.com/
PDF created with FinePrint pdfFactory Pro trial version www.pdffactory.com