APD DEMO P .APD.

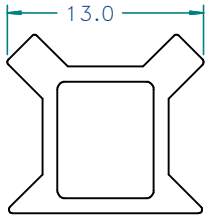

Vista superior
Escala 2:1

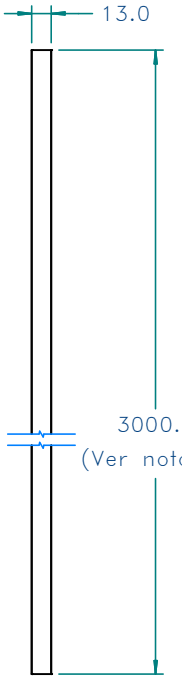

Vista frontal
Escala 1:5

PROVISIONAL HASTA:

NI-027-09

DISEÑO & DESARROLLO

Isometria
Escala 1:20

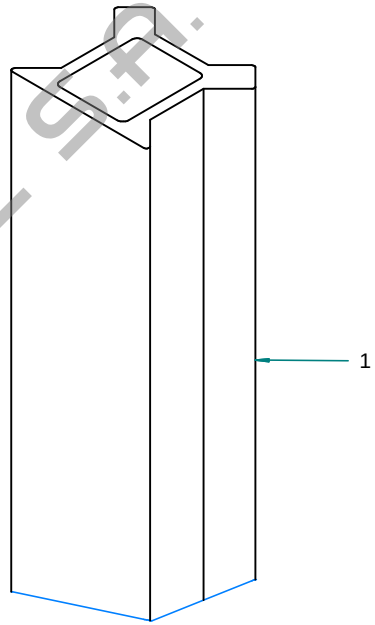

Detalle A
Escala 2:1

USO EXCLUSIVO DE MEPAL S.A.

Nota:
1. Cada perfil llega con esta longitud, cortarlo en obra de la misma altura del vidrio.

Plano No	Parte	Descripcion	Material	Cant	Observaciones
VTAC-010-004	1	Perfil policarbonato union en T	Policarbonato Ref. H2.770	1	Celda accesorios

LISTA DE PARTES

MEPAL
UNA EMPRESA CARVAJAL

FIRMA DE APROBACION

DIMENSIONES EN MILIMETROS
NO MEDIR SOBRE PLANO

DISEÑO: Diseño & Desarrollo — FECHA: 07/10/2008
DIBUJO: *Orlando Solis Cadena* — FECHA: 07/10/2008
ESCALA: Indicadas
ARCHIVO: VTAC050000

TOLERANCIAS NO INDICADAS	
DIMENSIONALES	± 1.0 mm
TROQUELADOS	± 0.2 mm
PERFORACIONES	± 0.2 mm
ANGULARES	± 1.0°
DESPUNTES	± 0.3 mm
PIVATIC - TRUMPF	± 0.2 mm

REVISION	NOTA DE ING.	FECHA	NOMBRE
00	086-08	2009-02-06	E.B.
01	027-09	2010-07-05	J.R.

LINEA: **VETRO**
TITULO: KIT UNION EN T
VIDRIO DE 10mm
ARMADA GENERAL
CODIGO: 22000009793
PLANO N°: VTAC-050-000 Rev01

LA INFORMACION TECNICA CONTENIDA EN ESTE PLANO ES PROPIEDAD DE MEPAL ESTA INFORMACION SOLO PUEDE SER USADA POR TERCEROS CON PREVIA AUTORIZACION ESCRITA DE MEPAL

PDF created with pdfFactory Pro trial version www.pdffactory.com