

Altura nominales	H<=204cm	H<=242cm	H<=280cm	H<=318cm
Codigo anonizado	22000017673	22000017674	22000017675	22000017676
Codigo pintado	22000104807	22000104808	22000104809	

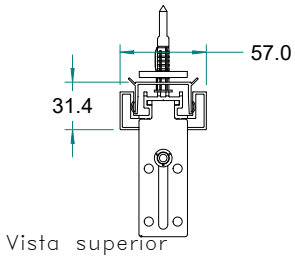


Vista superior

Escala 1:5

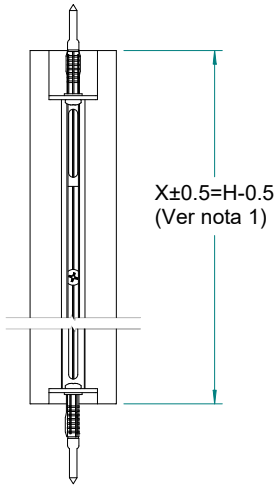


Vista frontal

Escala 1:5

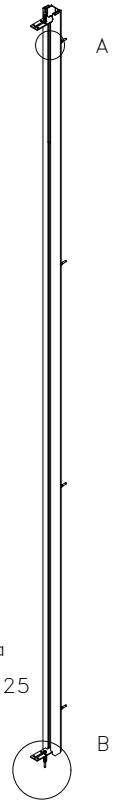

Isometria

Escala 1:25

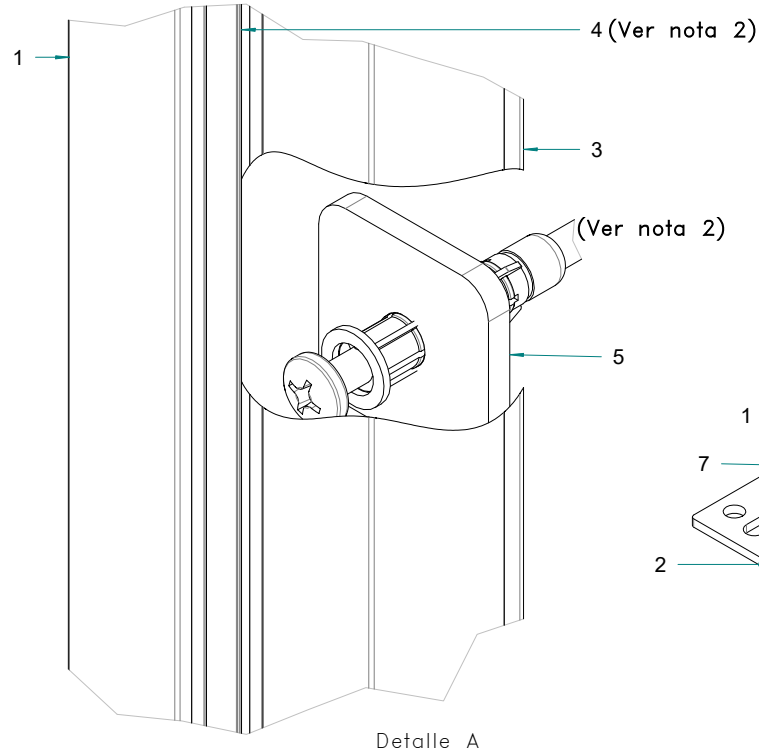


Detalle A

Escala 1:1

PROVISIONAL HASTA

NI-027-09

DISEÑO & DESARROLLO

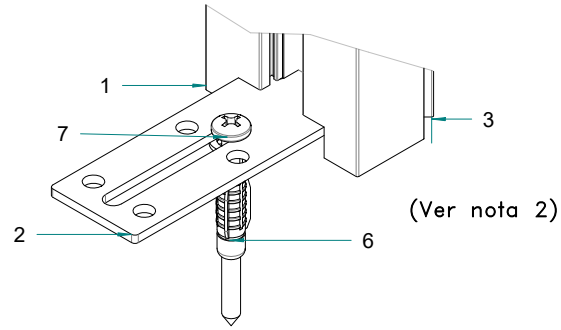

Detalle B

Escala 1:2

Nota:

1. La medida "H" corresponde a la altura del proyecto, y es suministrada por programación.
2. Para alturas mayores de 300cm duplicar estos elementos.

Plano No	Parte	Descripcion	Material	Cantidad	Observaciones
22000176	7	Tornillo 12 x 2 ½ cab. plana	Acero ASTM A36 / SAE 1020	6	Celda accesorios
22000193	6	Chazo plastico 5/16 x 1 1/2	Plastico Ref. PS-1612S	6	Celda accesorios
VTAC-060-020	5	Complemento	Lamina 4mm	4	Celda accesorios
VTAC-070-020	4	Empaque	Plastico coextruido	2	Celda accesorios
VTAC-010-001	3	Perfil llegadas	Plástico coextruido Ref. SI3302P0201	1	Celda accesorios
VTAC-060-030	2	Escuadra anclaje	Lamina 2.5mm	2	Celda accesorios
VTAC230010	1	Perfil llegada a pared	Aluminio REF. MEP-024	1	Celda accesorios

LISTA DE PARTES

Carvajal ESPACIOS

FIRMA DE APROBACIÓN

DIMENSIONES EN MILÍMETROS

NO MEDIR SOBRE PLANO

DESARROLLÓ: *Diseño & Desarrollo* FECHA: 7/10/2008

DIBUJÓ: *Orlando Solis Cadena* FECHA: 7/10/2008

ESCALA: Indicadas

ARCHIVO: VTAC230000

TOLERANCIAS NO INDICADAS

DIMENSIONALES	± 1.0 mm
TROQUELADOS	± 0.2 mm
PERFORACIONES	± 0.2 mm
ANGULARES	± 1.0°
DESPUNTES	± 0.3 mm
CNC	± 0.2 mm

REVISIÓN	NOTA DE ING.	FECHA	NOMBRE
01	027-09	2016-06-28	H.B.

LÍNEA: **VETRO**

TÍTULO: Kit llegada a pared
Vidrio de 10mm Armada general

CÓDIGO:

PLANO N°: VTAC230000

LA INFORMACIÓN TECNICA CONTENIDA EN ESTE PLANO ES PROPIEDAD DE CARVAJAL ESPACIOS S.A.S. ESTA INFORMACIÓN SOLO PUEDE SER USADA POR TERCEROS CON PREVIA AUTORIZACIÓN ESCRITA DE CARVAJAL ESPACIOS S.A.S.