

PROVISIONAL HASTA NI 002-26 / DISEÑO & DESARROLLO


| NOMINAL | H<=204cm | H<=242cm | H<=280cm | H<=318cm |
|---|---|---|---|---|
| 45,0cm | 22000017693 | 22000017694 | 22000017695 | 22000017696 |
| 60,0cm | 22000009775 | 22000009776 | 22000009777 | 22000009778 |
| 75,0cm | 22000009779 | 22000009780 | 22000009781 | 22000009782 |
| 90,0cm | 22000009783 | 22000009784 | 22000009785 | 22000009786 |
| 120,0cm | 22000009787 | 22000009788 | 22000009789 | 22000009790 |

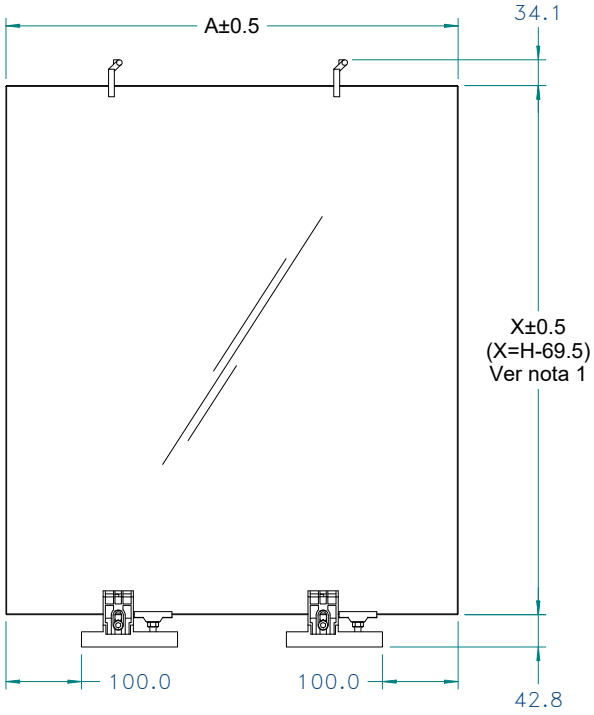



Vista frontal
Escala 1:12.5

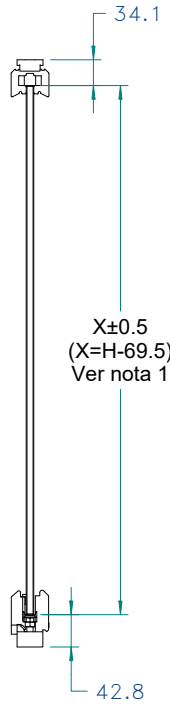


Vista lateral
Escala 1:12.5

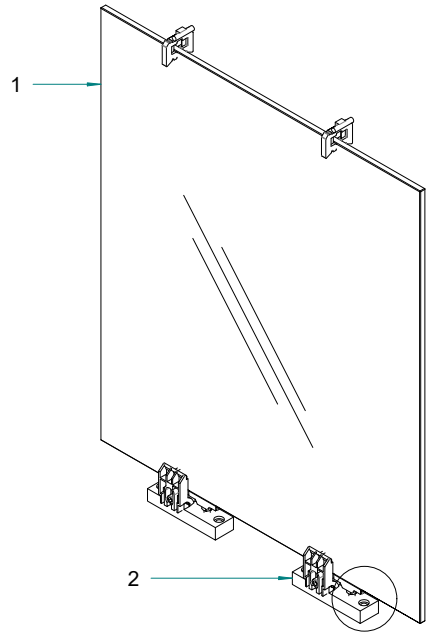


Isometria
Escala 1:10

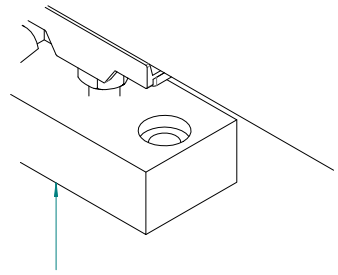


Detalle A
Escala 1:2

| | ANCHOS | | | | |
|---|---|---|---|---|---|
| NOMINAL | 45,0cm | 60,0cm | 75,0cm | 90,0cm | 120,0cm |
| A±0,5 | 447,5 | 597,5 | 747,5 | 897,5 | 1197,5 |

Nota:
1. La medida "H", corresponde a la altura del proyecto y debe ser suministrada por programacion.

| Plano No | Parte | Descripcion | Material | Cant | Observaciones |
|---|---|---|---|---|---|
| VTAC250000 | 2 | Kit sistema Nivelacion y Bloqueo pared | Varios | 2 | Celda accesorios |
| MPR-070-225 | 1 | Vidrio | Vidrio templado 10.0mm transparente | 1 | Celda carpinteria |

LISTA DE PARTES

Carvajal ESPACIOS

FIRMA DE APROBACIÓN

DIMENSIONES EN MILÍMETROS
NO MEDIR SOBRE PLANO

DESARROLLÓ: Diseño & Desarrollo — FECHA: 27/09/2008
DIBUJÓ: Orlando Solis Cadena — FECHA: 1/10/2008
ESCALA: Indicadas
ARCHIVO: VTPN020000

| TOLERANCIAS NO INDICADAS | |
|---|---|
| DIMENSIONALES | ± 1.0 mm |
| TROQUELADOS | ± 0.2 mm |
| PERFORACIONES | ± 0.2 mm |
| ANGULARES | ± 1.0° |
| DESPUNTES | ± 0.3 mm |
| CNC | ± 0.2 mm |

| REVISIÓN | NOTA DE ING. | FECHA | NOMBRE |
|---|---|---|---|
| 00 | 086-08 | 06-02-2009 | E.B. |
| 01 | 027-09 | 19-09-2013 | E.R. |
| 02 | 002-26 | 21-01-2026 | J.B. |

LÍNEA: VETRO
TÍTULO: Panel vidrio 45, 60, 75, 90 y 120cm
Armada general

CÓDIGO: INDICADOS
PLANO N°: VTPN020000

LA INFORMACIÓN TECNICA CONTENIDA EN ESTE PLANO ES PROPIEDAD DE CARVAJAL ESPACIOS S.A.S. ESTA INFORMACIÓN SOLO PUEDE SER USADA POR TERCEROS CON PREVIA AUTORIZACIÓN ESCRITA DE CARVAJAL ESPACIOS S.A.S.