

APD DEMO P .APD.

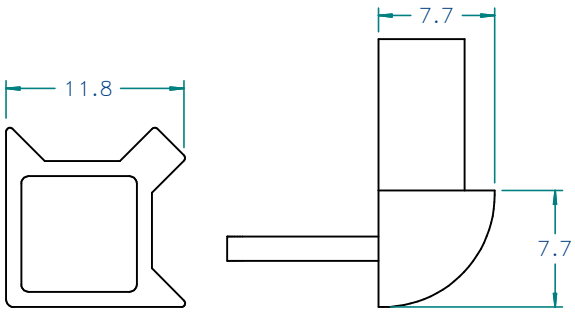


Vista superior
Escala 2:1

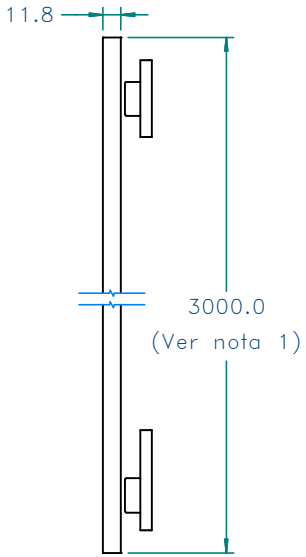


Vista frontal
Escala 1:5



Isometria
Escala 1:25

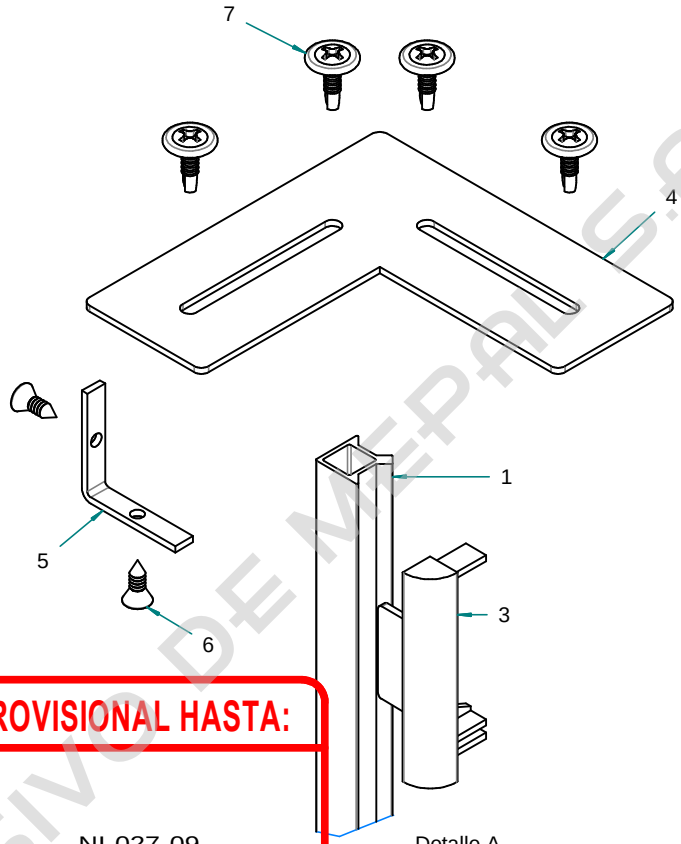

Detalle A
Escala 1:1

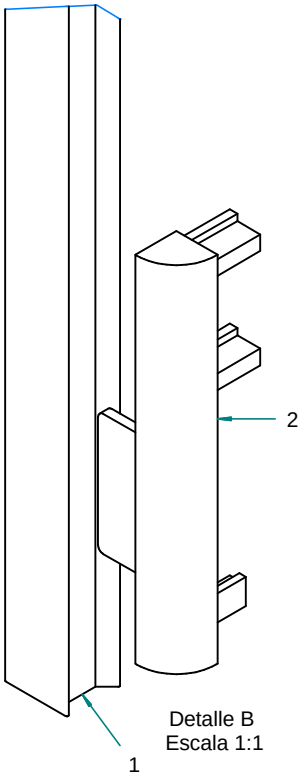

Detalle B
Escala 1:1

PROVISIONAL HASTA:

NI-027-09

DISEÑO & DESARROLLO

USO EXCLUSIVO DE MEPAL S.A.

Cod. 22000159	7	Tornillo autoperf.	Nº 8 x ½"	4	Celda accesorios
	6	Tornillo avell.N° 8 x 1-2	N° 8 x 1/2"	2	Celda accesorios
VTAC-040-020	5	Platina guia 90º	Lamina de 1.5mm	1	Celda accesorios
VTAC-040-010	4	Platina union a 90º	Lamina de 1.5mm	1	Celda accesorios
MPR-080-215	3	Puntera plástica giro 90° perfil techo	Plástico inyectado	1	Celda accesorios
MPR-080-214	2	Puntera plástica giro 90° zocalo inf.	Plástico inyectado	1	Celda accesorios
VTAC-010-003	1	Perfil policarbonato giros a 90°	Policarbonato	1	Celda accesorios
Plano No	Parte	Descripcion	Material	Canti	Observaciones

LISTA DE PARTES

Nota: 1- Cada perfil llega con esta longitud,
cortarlo en obra de la misma altura del vidrio.

MEPAL
UNA EMPRESA CARVAJAL

FIRMA DE APROBACION

DIMENSIONES EN MILIMETROS
NO MEDIR SOBRE PLANO

DISEÑO: Diseño & Desarrollo — FECHA: 07/10/2008
DIBUJO: *Orlando Solis Cadena* — FECHA: 07/10/2008
ESCALA: Indicadas
ARCHIVO: VTAC040000

TOLERANCIAS NO INDICADAS	
DIMENSIONALES	± 1.0 mm
TROQUELADOS	± 0.2 mm
PERFORACIONES	± 0.2 mm
ANGULARES	± 1.0°
DESPUNTES	± 0.3 mm
PIVATIC - TRUMPF	± 0.2 mm

REVISION	NOTA DE ING.	FECHA	NOMBRE
00	086-08	2009-02-06	E.B.
01	027-09	21-10-2009	D.O

LINEA: **VETRO**

TITULO: KIT UNION A 90°
VIDRIO DE 10mm
ARMADA GENERAL

CODIGO: 22000009792 — PLANO N°: VTAC-040-000 Rev01

LA INFORMACION TECNICA CONTENIDA EN ESTE PLANO ES PROPIEDAD DE MEPAL ESTA INFORMACION SOLO PUEDE SER USADA POR TERCEROS CON PREVIA AUTORIZACION ESCRITA DE MEPAL

PDF created with pdfFactory Pro trial version www.pdffactory.com