
PROVISIONAL HASTA NI 002-26 / DISEÑO & DESARROLLO


ALTURA NOMINAL	H<=204cm	H<=242cm	H<=280cm	H<=318cm
CODIGO	22000010922	22000010923	22000010924	22000010925




VISTA SUPERIOR
ESCALA 1:15

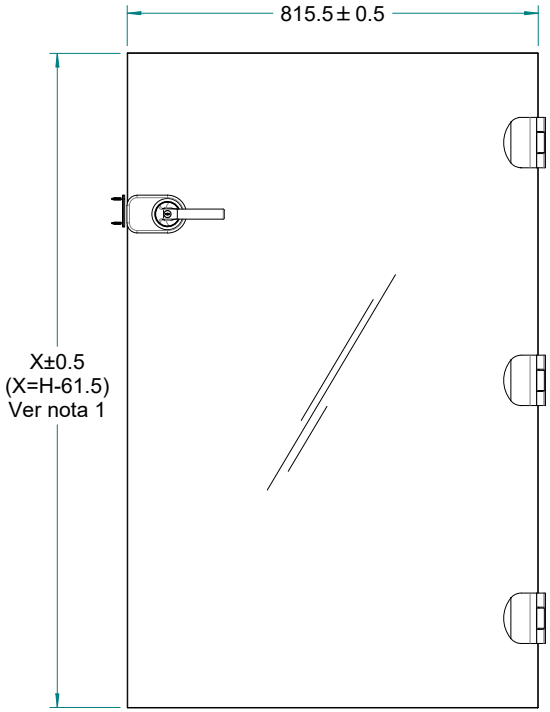


VISTA FRONTAL
ESCALA 1:15

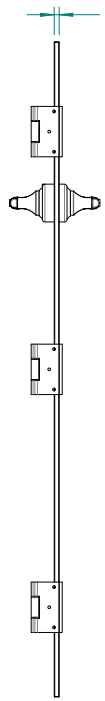

VISTA LATERAL
ESCALA 1:15

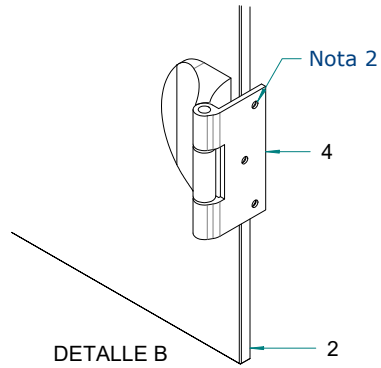

DETALLE B
ESCALA 1:5

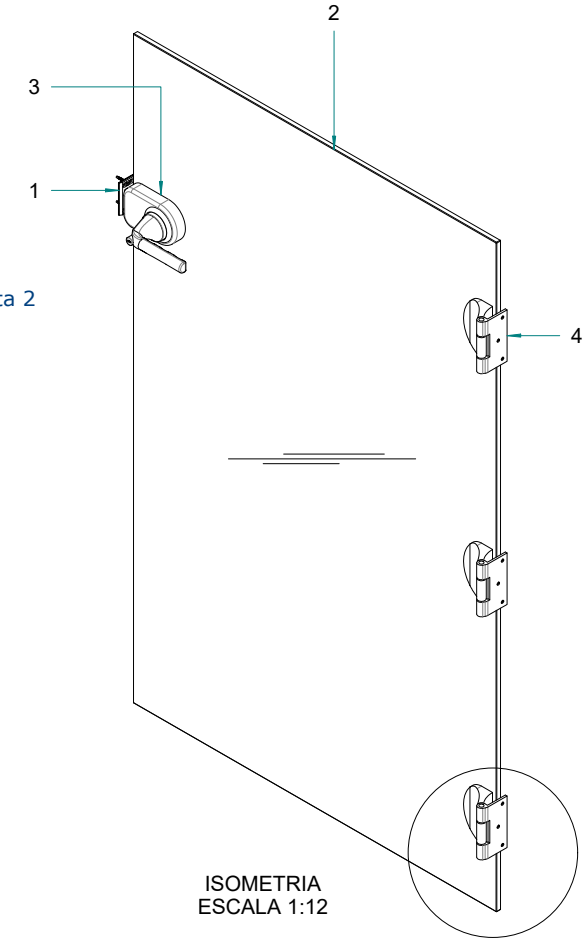

ISOMETRIA
ESCALA 1:12

B

Plano No	Parte Nº	Descripcion	Material	Cant	Observaciones
22005938	4	Bisagra	Varios	3	Celda accesorios
22005527	3	Cerradura HOPPE	Varios	1	Celda accesorios
MPR-070-227	2	Vidrio puerta	Vidrio templado 10.0mm transparente	1	Ensamble puertas
VTPT010010	1	Recibidor cerradura	Varios	1	Celda accesorios

LISTA DE PARTES

Nota:
1- H corresponde a la altura del proyecto y es determinada por programacion.
2- Cada bisagra incluye 3 tornillos Nº 8x1" avell. autoperforante.

Carvajal ESPACIOS

FIRMA DE APROBACIÓN

DIMENSIONES EN MILÍMETROS
NO MEDIR SOBRE PLANO

DESARROLLÓ: *Diseño & Desarrollo* FECHA: 10/09/2008
DIBUJÓ: *Orlando Solis Cadena* FECHA: 26/01/2009
ESCALA: Indicadas
ARCHIVO: VTPT010000

TOLERANCIAS NO INDICADAS	
DIMENSIONALES	± 1.0 mm
TROQUELADOS	± 0.2 mm
PERFORACIONES	± 0.2 mm
ANGULARES	± 1.0°
DESPUNTES	± 0.3 mm
CNC	± 0.2 mm

REVISIÓN	NOTA DE ING.	FECHA	NOMBRE
00	086-08	06-02-2009	E.B.
01	027-09	07-12-2016	R.B
02	002-26	20-01-2026	J.B

LÍNEA: **VETRO**
TÍTULO: Nave puerta vidrio de 90cm
Armada general

CÓDIGO: INDICADOS
PLANO N°: VTPT010000

LA INFORMACIÓN TECNICA CONTENIDA EN ESTE PLANO ES PROPIEDAD DE CARVAJAL ESPACIOS S.A.S. ESTA INFORMACIÓN SOLO PUEDE SER USADA POR TERCEROS CON PREVIA AUTORIZACIÓN ESCRITA DE CARVAJAL ESPACIOS S.A.S.